


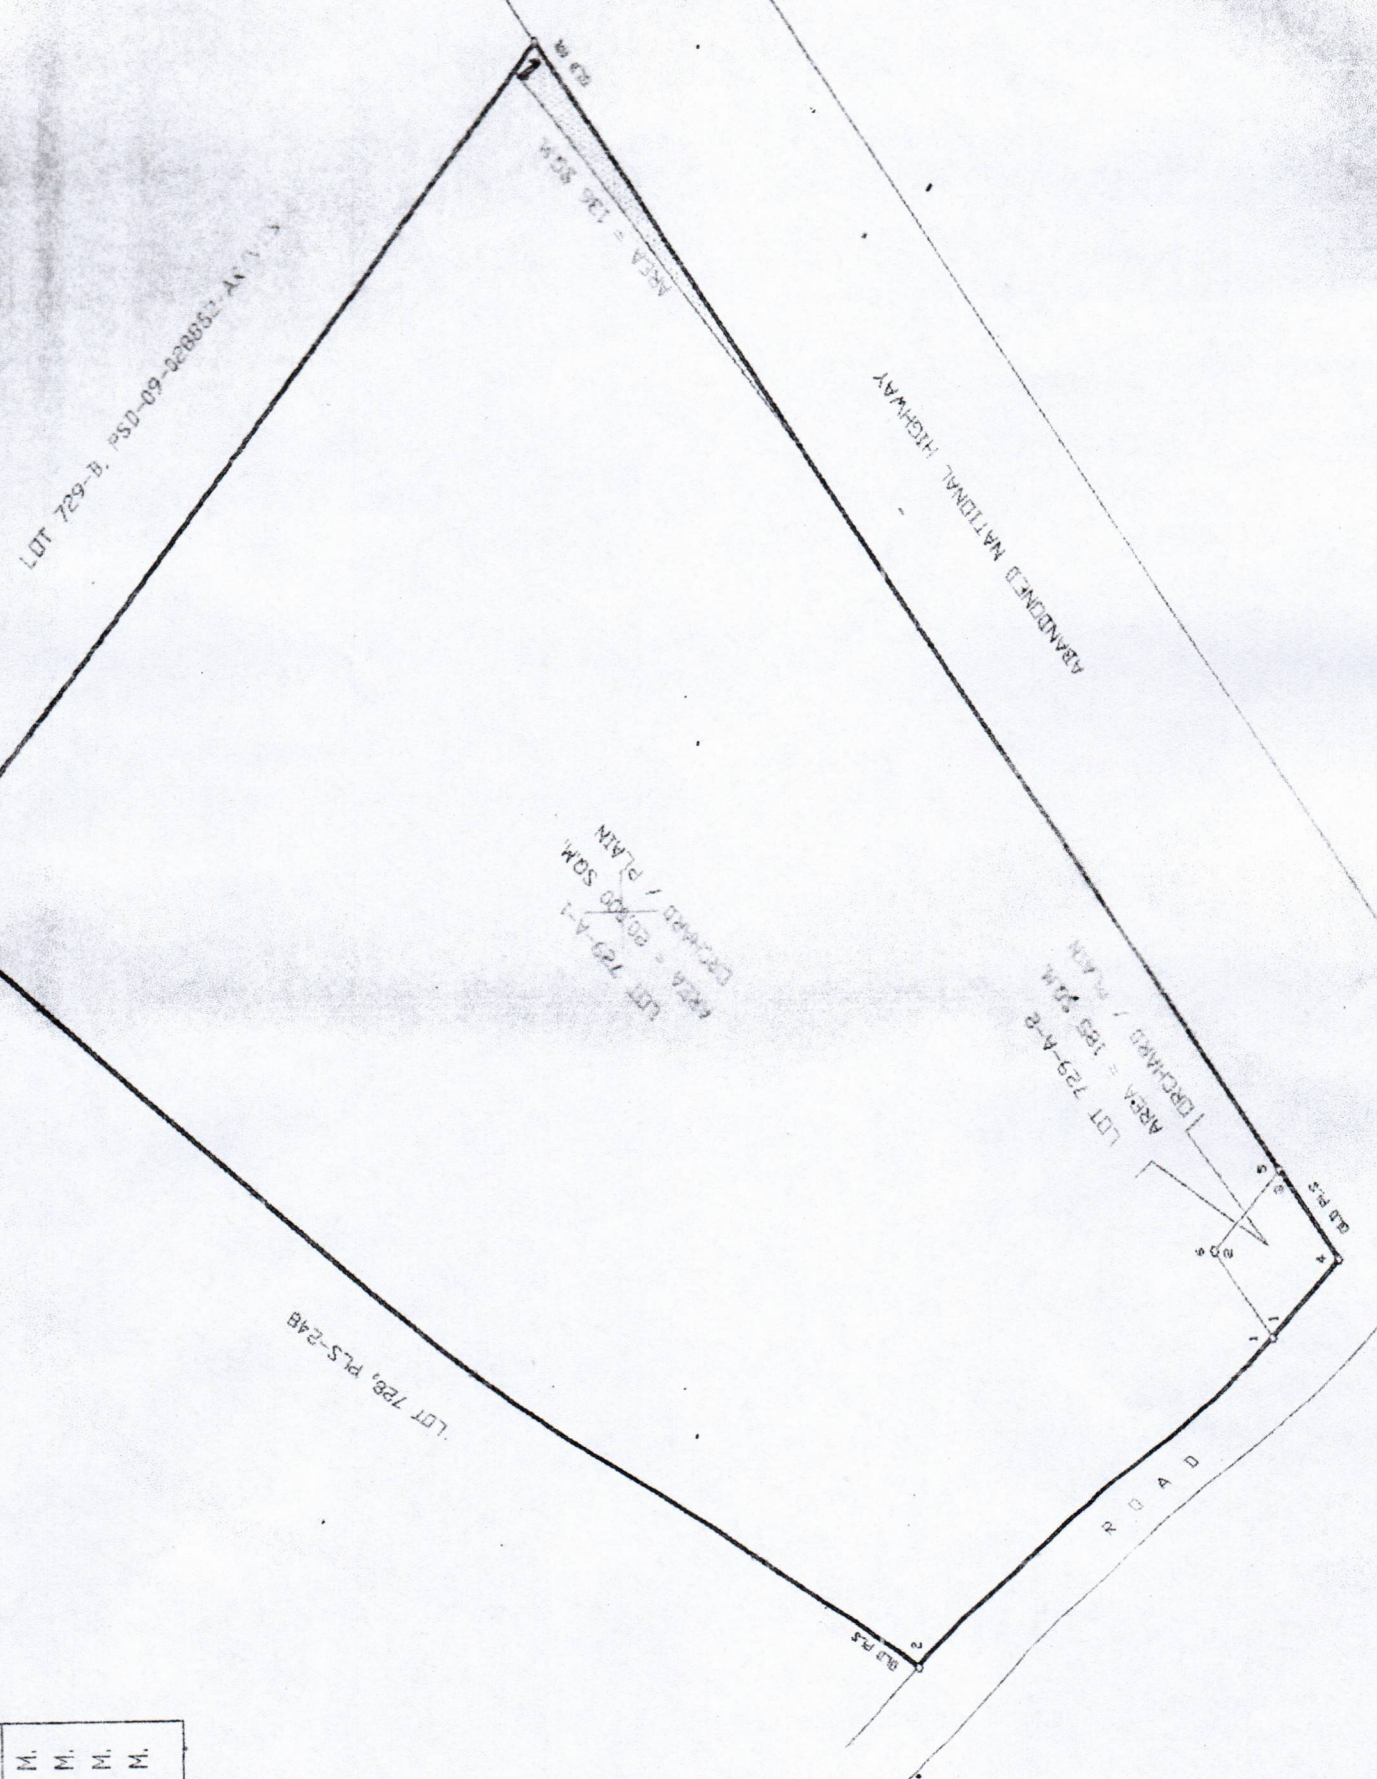

1	M.
1	M.
1	M.
1	M.
1	M.

TECHNICAL DESCRIPTIONS

SURVEY PLAN : PSD-9-095794
 LOT NO. : LOT 729-A-1
 PORTION OF : LOT 729-A, PSD-09-028862-AR/VOS
 LOCATION : BARANGAY OF SANITO, IPIL, ZAMBO. SIBUGAY
 BOUNDARIES :

LINE	BEARINGS	REMARKS
1-2	SW	ROAD
2-3	NW	LOT 728, PLS-248
3-4	NE	LOT 729-B, PSD-09-028862-AR/VOS
4-5	SE	ABANDONED NATIONAL HIGHWAY
5-6-1	SE	LOT 729-A-2, PSD-9-095794.

TIE POINT: BLLM NO. 22, PLS - 248
 LOT DESCRIPTIONS:

LINE	BEARINGS	DISTANCES
TIE POINT TO COR. 1	S. 24 DEG. 27'E.,	2636.86 M.
1-2	N. 45 DE. 07'W.,	72.31 M.
2-3	N. 27 DEG. 04'E.,	180.00 M.
3-4	S. 47 DEG. 21'E.,	137.15 M.
4-5	S. 53 DEG. 06'W.,	171.94 M.
5-6	N. 45 DEG. 09'W.,	13.74 M.
6-1	S. 53 DEG. 06'W.,	13.60 M.

AREA: TWENTY THOUSAND (20,000) sq. m.

DESCRIPTIONS OF CORNERS: CORNER 2 BY OLD PLST CYL. CONC. MONS. 15 X 60 CMS., CORNERS 3,4 BY OLD AR CYL. CONC. MONS. 15 X 40 CMS., AND THE REST BY PS CYL. CONC. MONS. 15 X 50 CMS.

BEARINGS: TRUE

DATE OF ORIGINAL SURVEY: JAN. 18, 1941

DATE OF SUBDIVISION SURVEY: APRIL 11, 2024

DATE OF APPROVED: MAY 15, 2024

GEODETIC ENGINEER: ENGR. ASHRAF T. GULDAM

PREPARED AND VERIFIED BY:

ENGR. ASHRAF T. GULDAM
 Geodetic Engineer
 PRC No. 3875 dated 03-08-1993

CERTIFIED CORRECT:
 For the Chief, Surveys and Mapping Division:

ENGR. ARLYN E. SALPURA-HIOLEN
 Chief, Technical Services Unit

TD CERT. FEE OF PHP 6.00 PAID UNDER OR NO. 2481163

DTD. 09-21-2023

TECHNICAL DESCRIPTIONS

SURVEY PLAN : PSD-9-095794
 LOT NO. : LOT 729-A-1
 PORTION OF : LOT 729-A, PSD-09-028862-AR/VOS
 LOCATION : BARANGAY OF SANITO, IPIL, ZAMBO. SIBUGAY
 BOUNDARIES :

LINE	BEARINGS	REMARKS
1-2	SW	ROAD
2-3	NW	LOT 728, PLS-248
3-4	NE	LOT 729-B, PSD-09-028862-AR/VOS
4-5	SE	ABANDONED NATIONAL HIGHWAY
5-6-1	SE	LOT 729-A-2, PSD-9-095794.

TIE POINT: BLLM NO. 22, PLS - 248
 LOT DESCRIPTIONS:

LINE	BEARINGS	DISTANCES
TIE POINT TO COR. 1	S. 24 DEG. 27'E.,	2636.86 M.
1-2	N. 45 DE. 07'W.,	72.31 M.
2-3	N. 27 DEG. 04'E.,	180.00 M.
3-4	S. 47 DEG. 21'E.,	137.15 M.
4-5	S. 53 DEG. 06'W.,	171.94 M.
5-6	N. 45 DEG. 09'W.,	13.74 M.
6-1	S. 53 DEG. 06'W.,	13.60 M.

AREA: TWENTY THOUSAND (20,000) sq. m.

DESCRIPTIONS OF CORNERS: CORNER 2 BY OLD PLS CYL. CONC. MONS. 15 X 60 CMS., CORNERS 3,4 BY OLD AR CYL. CONC. MONS. 15 X 40 CMS., AND THE REST BY PS CYL. CONC. MONS. 15 X 50 CMS.

BEARINGS: TRUE

DATE OF ORIGINAL SURVEY: JAN. 18, 1941

DATE OF SUBDIVISION SURVEY: APRIL 11, 2024

DATE OF APPROVED: MAY 15, 2024

GEODETIC ENGINEER: ENGR. ASHRAF T. GULDAM

PREPARED AND VERIFIED BY:

ENGR. ASHRAF T. GULDAM
 Geodetic Engineer
 PRC No. 3875 dated 03-08-1993

CERTIFIED CORRECT:
 For the Chief, Surveys and Mapping Division:

ENGR. ARLYN E. SALPURA-HIOLEN
 Chief, Technical Services Unit

TD CERT. FEE OF PHP 6.00 PAID UNDER OR NO. 2481163 DTD. 09-21-2023

TAX DECLARATION OF REAL PROPERTY

Prop. Ty Identification No.

080-05-0010-002- 38

TIN:

Tel No

TIN:

Tel No

ZAMBOANGA SIBUGAY

IRIL

(Municipality Province/City)

FSD-09-028059-AR/VOS

Survey No

Lot No 729-A

BLK No.

South

West

SW-ALONG LINE 1-2 BY ROAD

NW-ALONG LINE 2-5 BY LOT 720

W. Shirey

D. of Description:

C. No.

Specify:

Actual Area

Assessment Level

Assessed Value

40

10

Pho

19,120.00

Pho

19,120.00

Fourteen thousand, one hundred twenty Pesos and 00/100
(Amount in Words)

Effectivity of Assessment/Reassessment:

Qtr.

2013
Yr.

7/11/2012

Date

ARCELINO BRACAMONTE, CPA
ACLR Provincial Assessor

7/11/2012

Date

Previous Owner: E. BEN CAROLLET

Previous A.V. Pho

19,120.00

TRANSFERRED BY DEED NO. 1576 DATED 7/11/12 ISSUED AT ZATO IS. SERVICE FEE 50.00 PAID PER OR
NOTARIAL POWER OF ATTORNEY NO. 1576 DATED 7/11/12 ISSUED AT ZATO IS. TRANSFERRED BY TRANSFER CERT. OF TITLE NO. T-57 140 ISSUED BY
NOTARIAL POWER OF ATTORNEY NO. 1576 DATED 7/11/12.

This Declaration is for real property taxation purposes only and the situation indicated herein are based on the schedule of land market value prepared for the purpose and is hereby enacted into an Ordinance by the Sangguniang Panglungsod.

OFFICIAL RECEIPT

Province of ZAMBOANGA SIBUGAY

ORIGINAL

0539917

PREVIOUS TAX RECEIPT NO.

CASEL

FOR THE YEAR

DATE 9-11-23

REMARKS

NAME OF

DEED NO.

DATE

NOTARIAL

POWER OF

ATTORNEY

NO.

DATE

ISSUED

AT

ZATO IS.

TRANSFERRED

BY

DEED NO.

DATE

ISSUED

AT

ZATO IS.

TRANSFERRED

BY

DEED NO.

DATE

ISSUED

AT

ZATO IS.

REAL PROPERTY TAX

Block & Lot No.

Tax No.

Assessed Value

Block & Lot No.

Tax No.

Assessed Value

TOTAL

Municipal Treasurer

Provincial Treasurer

LINE BEING S. 24° 33' E.; C. 649.81 M.
 L.M. NO. 22, PLS-248.

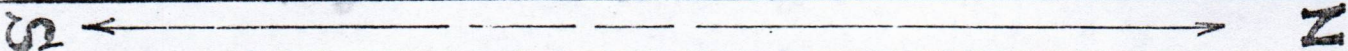

OF DOT 720-A, FSD-09-02B86C-A1/Ve

AS PREPARED FOR

EILEEN CAINGLET

SITUATED IN THE

PARANGAY OF PANGI
MUNICIPALITY OF IPIL
PROVINCE OF ZAMBOANGA SIBUGAY
ISLAND OF MINDANAO
CONTAINING AN AREA OF 20,185 SQ

WEARING: TRUE
SCALE: 1:6000

CERTIFICATION

I hereby certify that this is the true and correct sketch plan of the land herein as per Technical Description appearing in Owner's Duplicate Certificate of T. C. 1
E-39, 255.

FAMIL H. MARKS JR
GEODETIC ENGINEER

Reg. Cert. No. 4003 Dated: 07-18-04
F.T.R. No. 1743058 Dated: 01-16-09

(CONTINUATION OF TECHNICAL DESCRIPTION)
MEMORANDUM OF ENCUMBRANCES

(When necessary use this page for the continuation of the technical description)

Entry No.

1-2 N. 45 deg., 07°W., 86.02 m.
2-3 N. 37 deg., 04°E., 180.00 m.
3-4 S. 47 deg., 21°E., 137.15 m.
4-1 S. 53 deg., 06°W., 185.54 m.

Bearings

: True

Area

: TWENTY THOUSAND ONE HUNDRED EIGHTY FIVE

Title No.

: E-19, 193

Original lot No.

: Lot 729

Survey No.

: File 248, Ipil Public Land Subd.

Date of Survey

: March 31, 1956

Date of Approval

: July 14, 1957

Geodetic Engineer

: Romoganes A. Alarín

Description of Corners

: Corners 1, 2 by Old 2 1/2" cyl. conc. mons. 15 x 60
cm., & the rest by 1 1/2" cyl. conc. mons. 15 x 40
cm.

REGISTRY OF DEEDS FOR THE PROVINCE OF ZAMBOANGA DEL SUR

No. 1-57, 140

A portion of land comprising approximately 100 hectares, situated at Pangri, Ipil, Province of Zamboanga, Island of Mindanao. Bounded on the NE., along line 3-4, Lot 728-3, Td-09-0283-2-ar/ves, on the SE., along line 4-1, National Highway (60.00 m. wide), on the SW., along line 1-2, road, on the NW., along line 2-3, lot 728, Pls-243, Ipil Public Land Subdivision. Beginning at a point marked "1" on plan being S. 24 deg. 30' E., 2,649.81 m. from BLM NO. 22, Pls-248.

as owner thereof, in fee simple, subject to such of the encumbrances mentioned in Section 44 of said Decree as may be subsisting, and to subject parcel of land was previously issued a Certificate of Land Ownership Award (CLOA) bearing number 00365196.

This certificate is a transfer from Transfer Certificate of Title No. 1-9-28, which is cancelled by virtue hereof in so far as the above-described land is concerned.

Entered at Sancti Spiritus del Sur
Philippines, on the 21st day of December
in the year two thousand and ten
at 1:01 m.

ATTEST:

Urgello St., Cebu City, Philippines
(Owner's postal address)

ATTY. RICARDO E. DIOSO, JR.
(Register of Deeds)

*State the civil status, name of spouse if married, age if a minor, citizenship and residence of the registered owner. If the owner is a married woman, state also the citizenship of her husband. If the land is registered in the name of the conjugal partnership, state the citizenship of both spouses.